PROYECTO ARQUITECTÓNICO

EDIFICIO DE VIVIENDAS

Av. Paseo Colon 735

San Telmo - Ciudad de Buenos Aires

DOCUMENTACIÓN

01 PLANTAS

02 VISTAS

03 RENDERS

04 ANÁLISIS DE SUPERFICIES

CANEVA

ARQUITECTOS

AGOSTO 2026

BUENOS AIRES



CANEVA

ARQUITECTOS

PROYECTO
Av. Paseo Colon 735

OBRA
Edificio de Viviendas

UBICACIÓN
San Telmo


PLANO
Render

ESCALA
S/Esc

FECHA
12/08/2026

PLANO N°
A - 01

REVISIÓN
R00

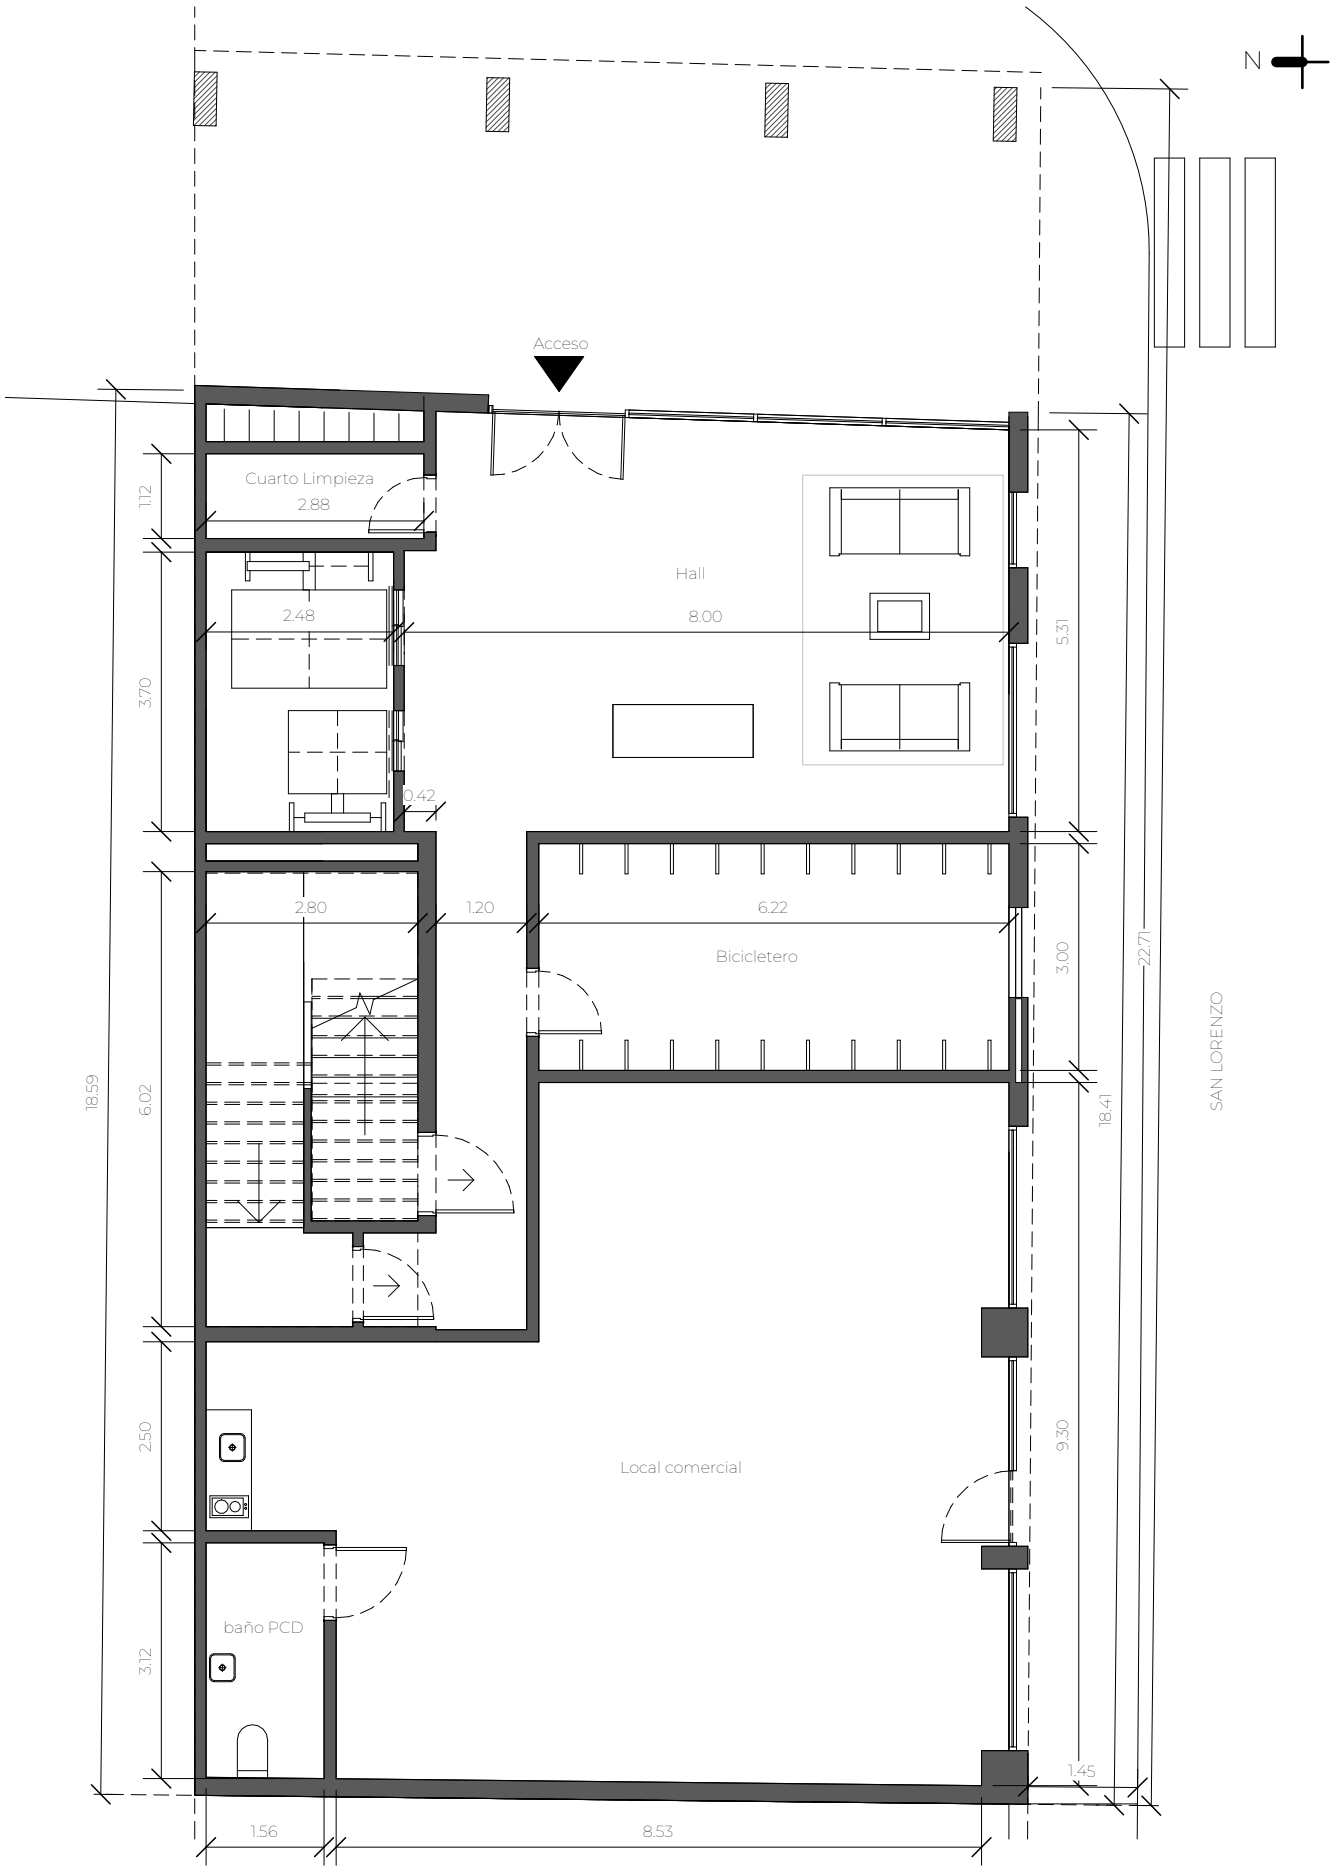

CANEVA

ARQUITECTOS

PROYECTO
Av. Paseo Colon 735

OBRA
Edificio de Viviendas

UBICACIÓN
San Telmo


PLANO
Planta PB - Completa

ESCALA
1:100

FECHA
12/08/2026

PLANO N°
A - 02

REVISIÓN
R00

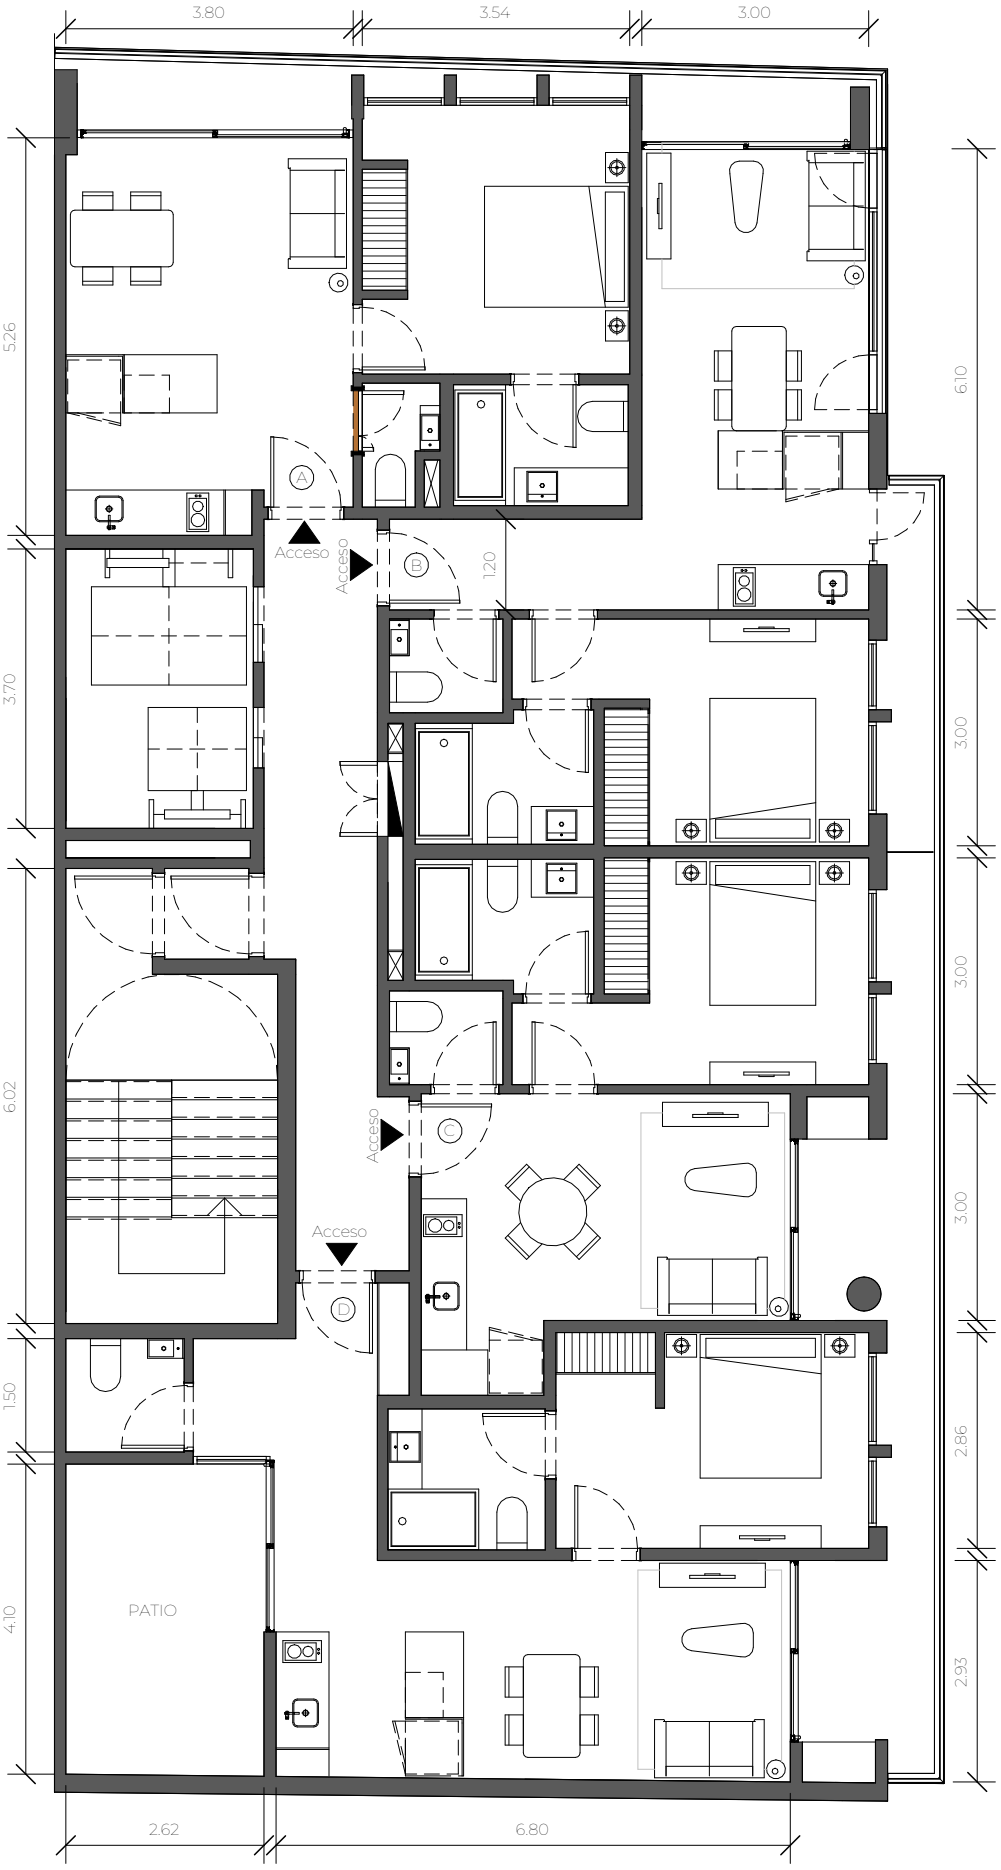

CANEVA

ARQUITECTOS

PROYECTO
Av. Paseo Colon 735

OBRA
Edificio de Viviendas

UBICACIÓN
San Telmo


PLANO
Planta 1° - Completa

ESCALA
1:100

FECHA
12/08/2026

PLANO N°
A - 03

REVISIÓN
R00

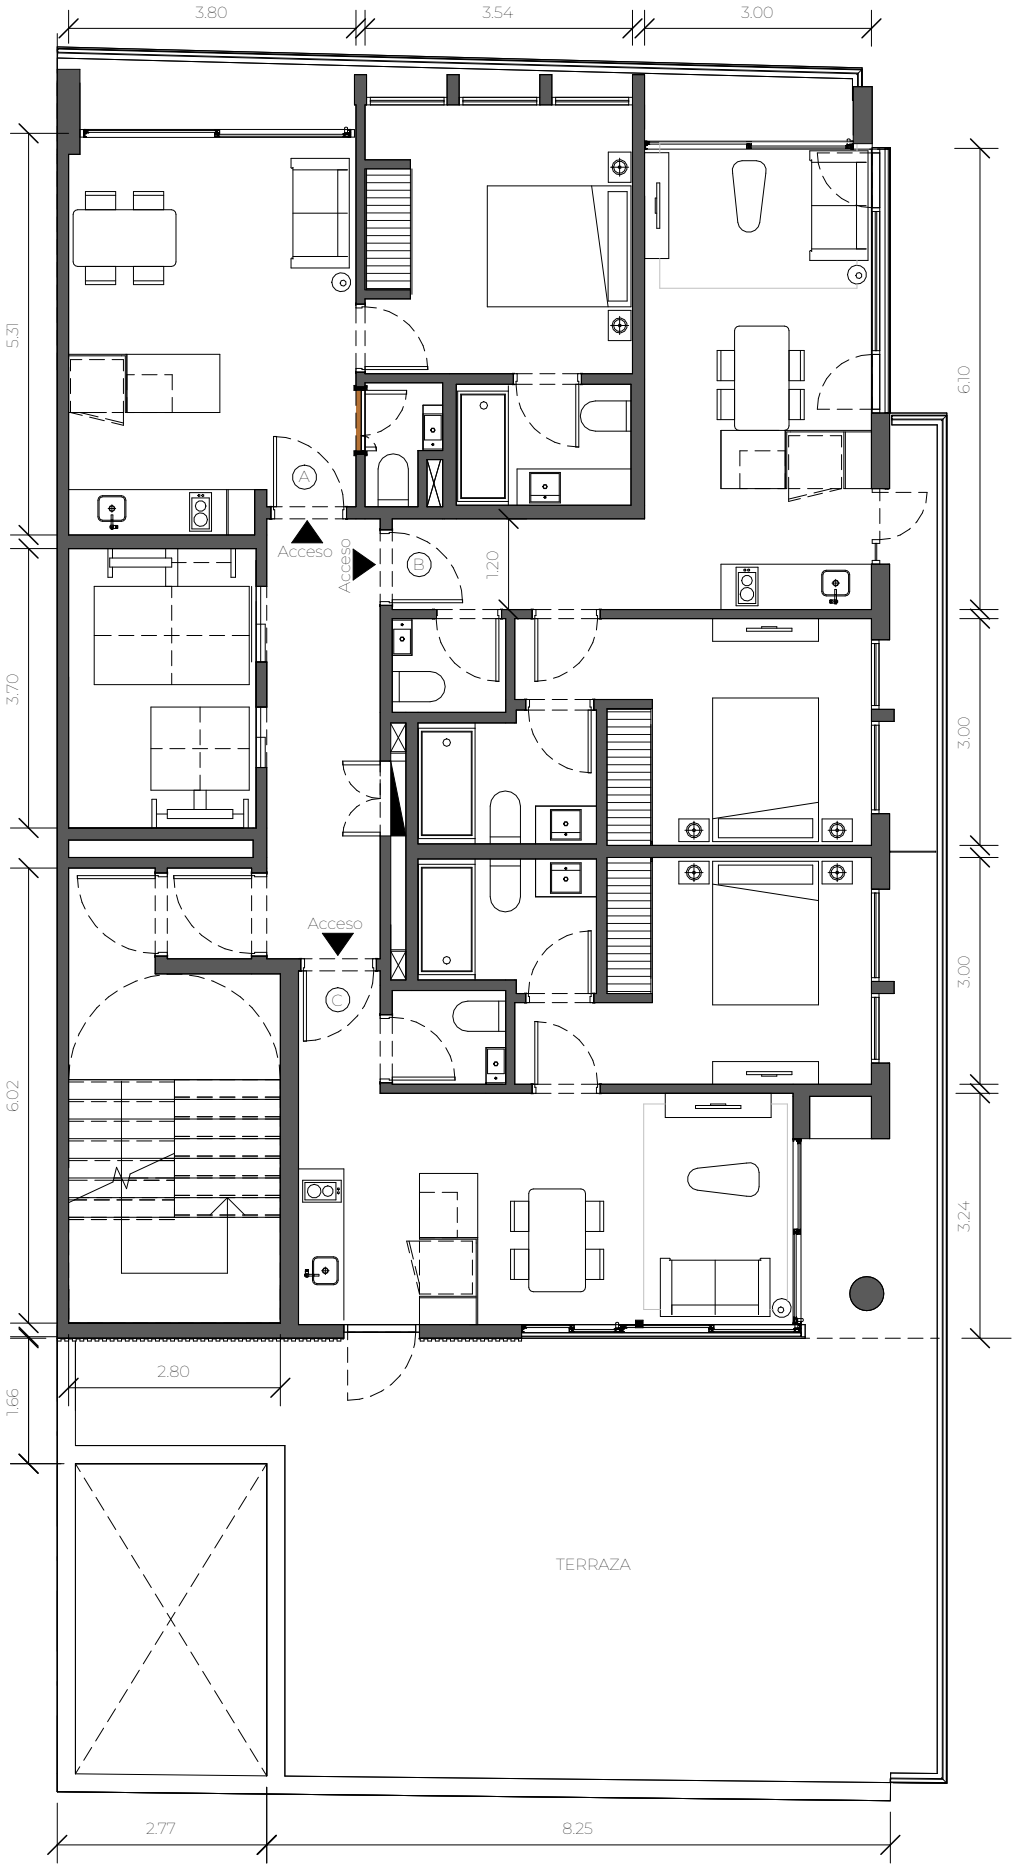

CANEVA

ARQUITECTOS

PROYECTO
Av. Paseo Colon 735

OBRA
Edificio de Viviendas

UBICACIÓN
San Telmo


PLANO
Planta 2° - Completa

ESCALA
1:100

FECHA
12/08/2026

PLANO N°
A - 04

REVISIÓN
R00

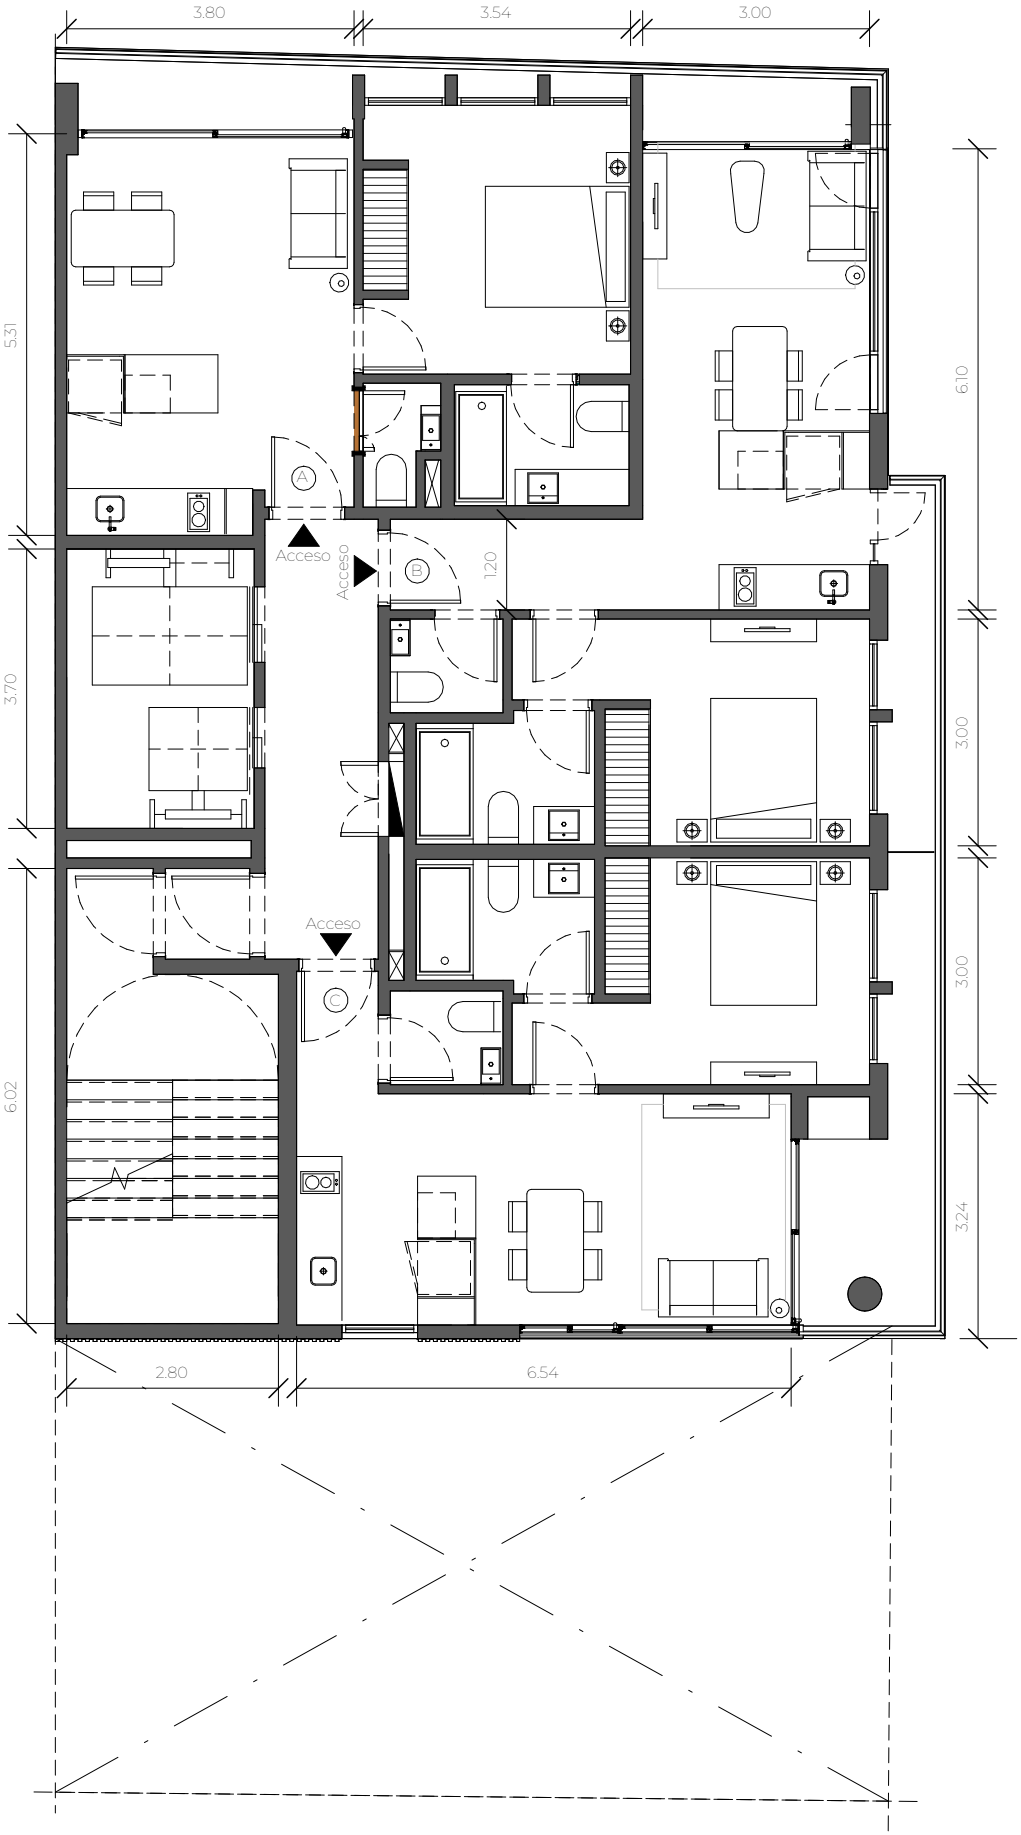

CANEVA

ARQUITECTOS

PROYECTO
Av. Paseo Colon 735

OBRA
Edificio de Viviendas

UBICACIÓN
San Telmo


PLANO
Planta 3°/12° - Completa

ESCALA
1:100

FECHA
12/08/2026

PLANO N°
A - 05

REVISIÓN
R00

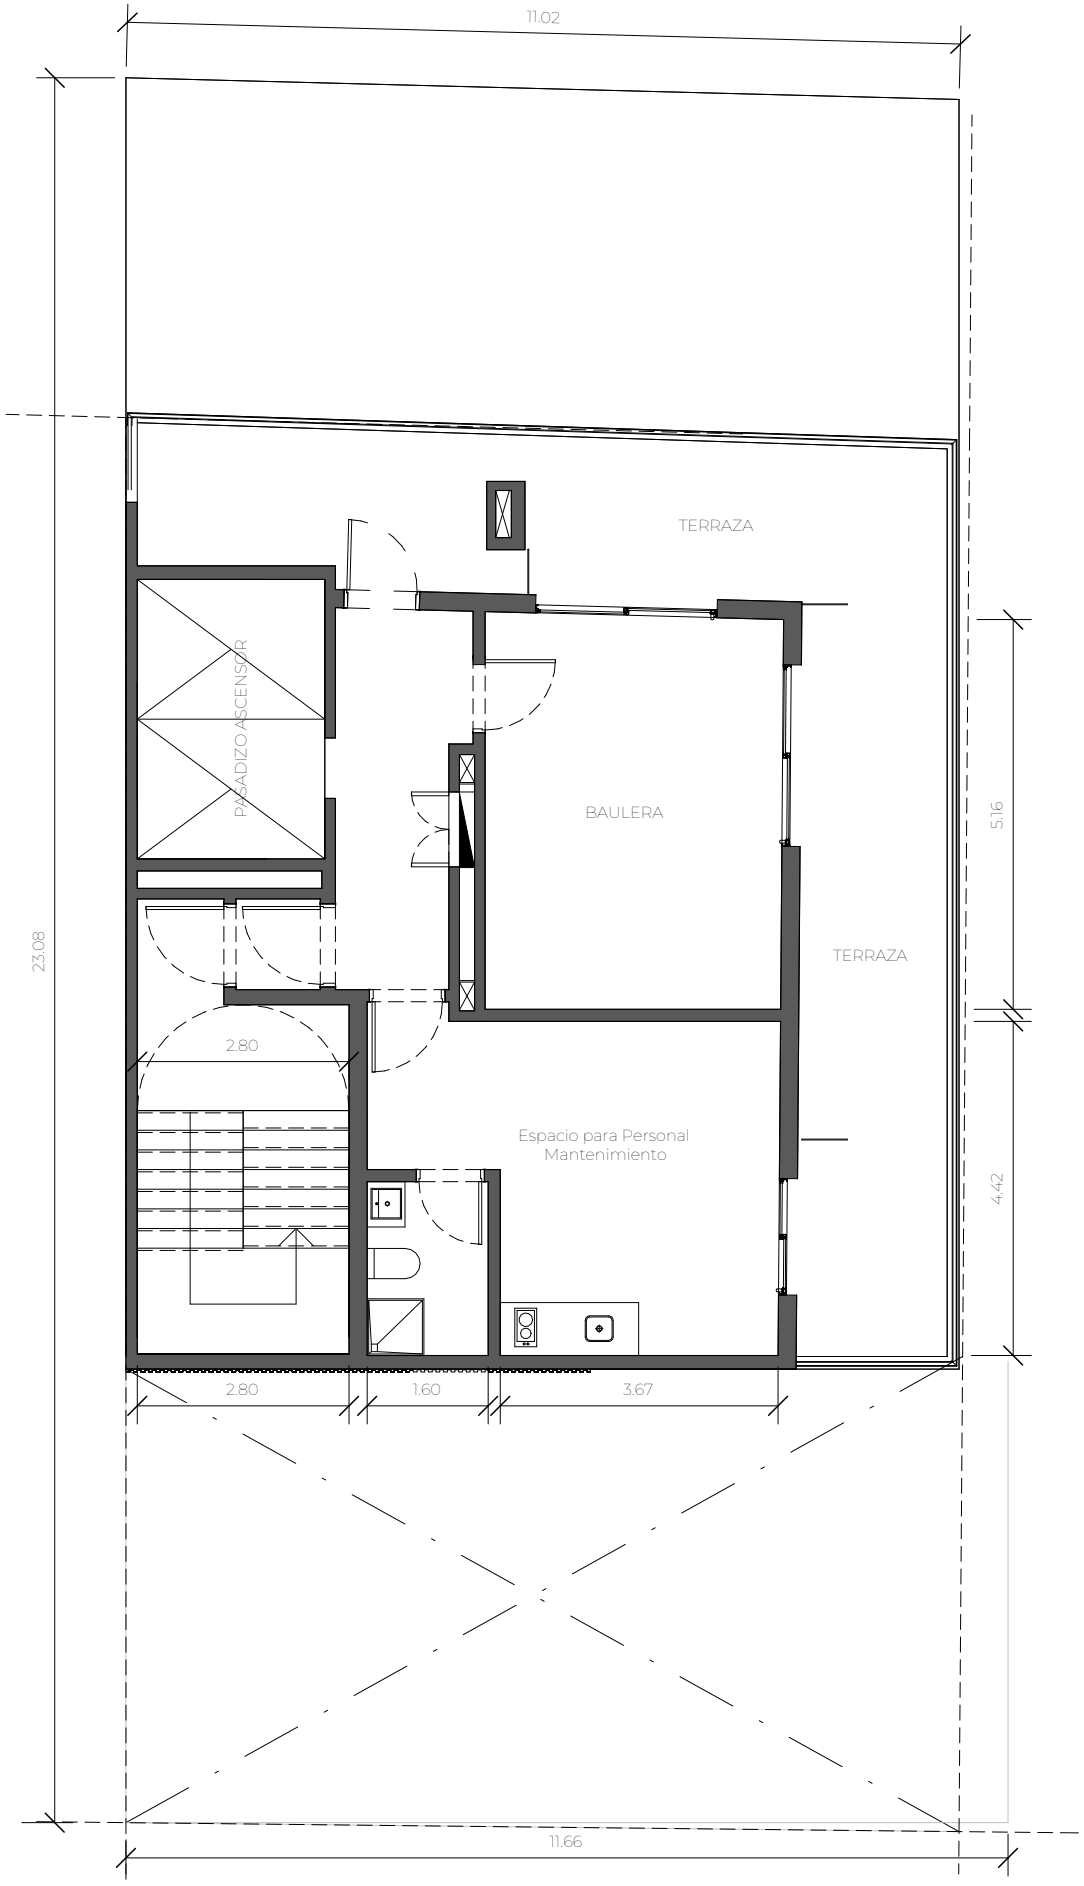

CANEVA

ARQUITECTOS

PROYECTO
Av. Paseo Colon 735

OBRA
Edificio de Viviendas

UBICACIÓN
San Telmo


PLANO
Planta 13° - Completa


ESCALA
1:100

FECHA
12/08/2026

PLANO N°
A - 06

REVISIÓN
R00

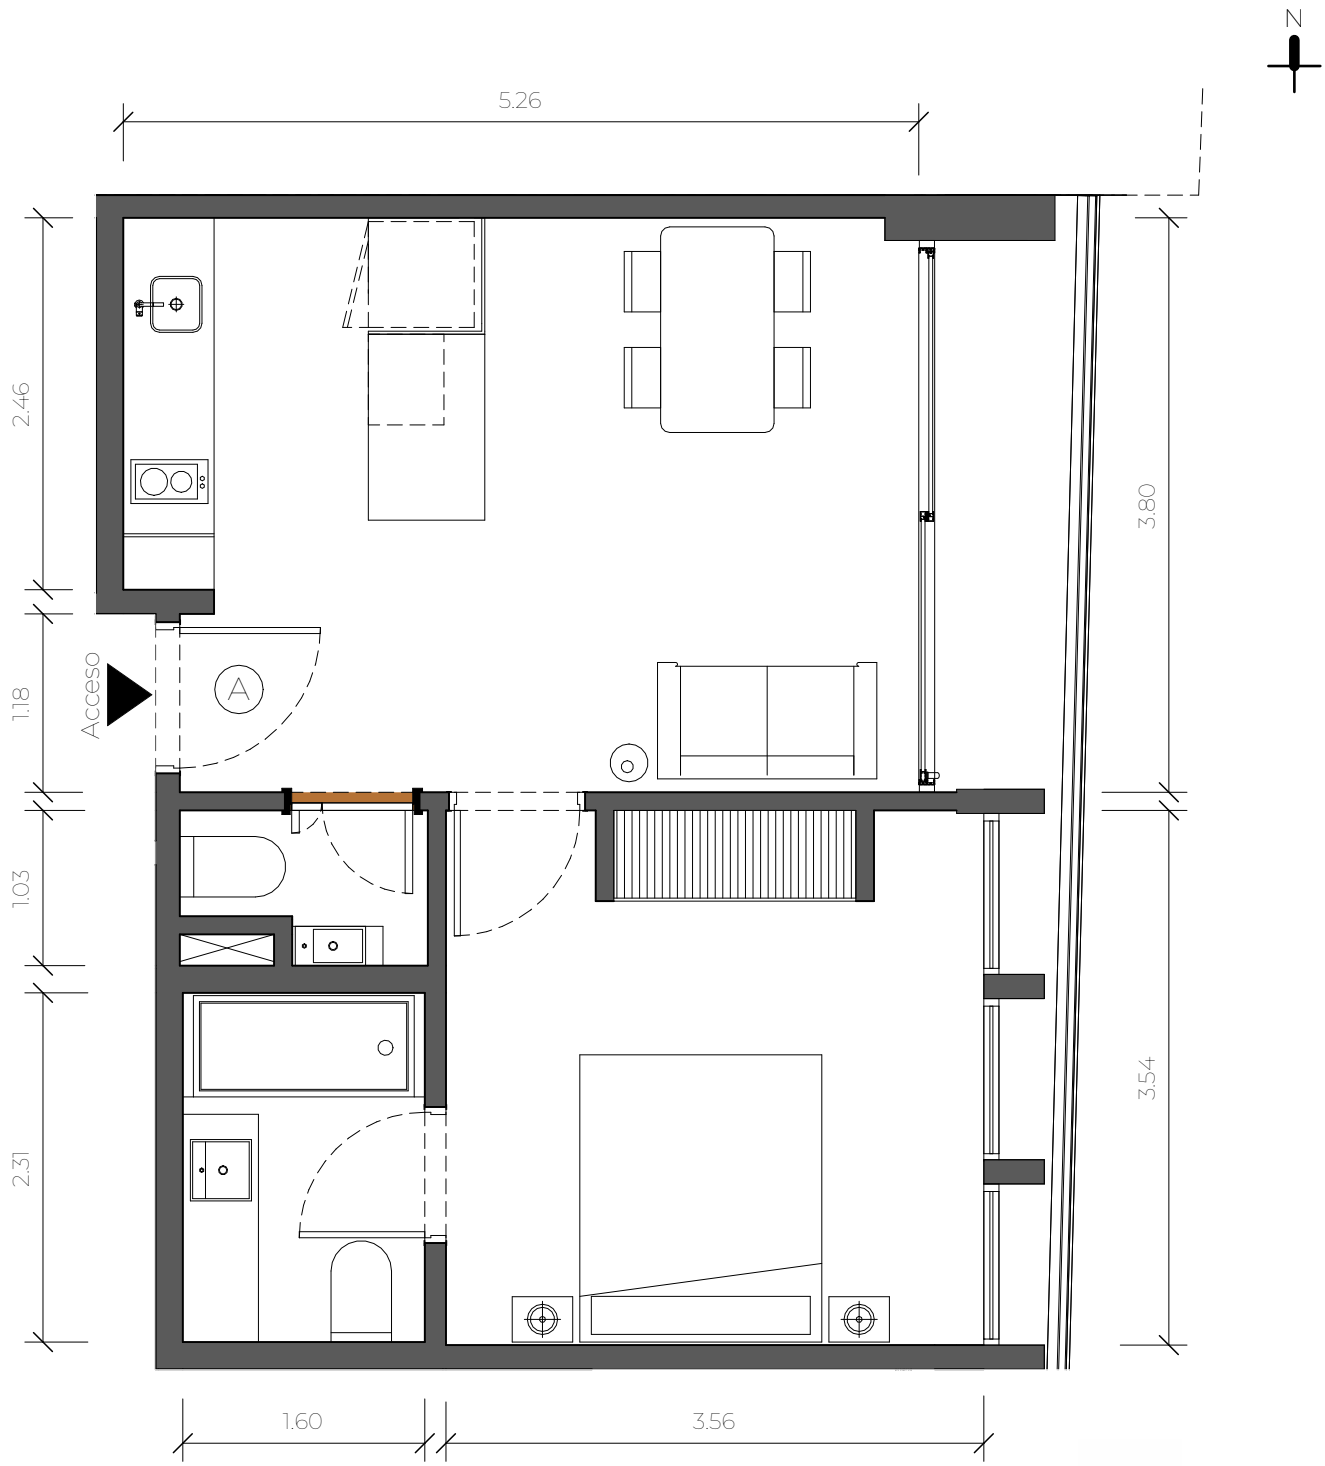

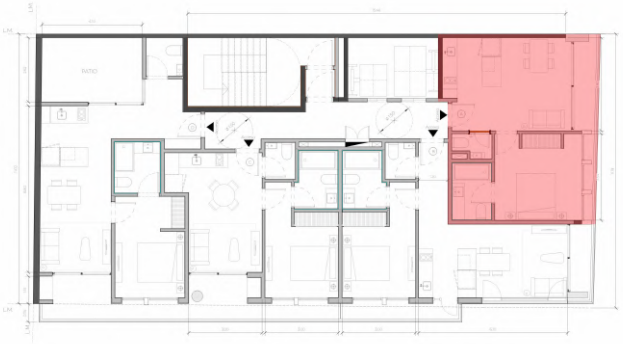

- Sup. cubierta: 41.0 m2
- Sup. semi cubierta: 6.7 m2

- Sup. Total: 47.7 m2

Cantidad: 12

CANEVA
ARQUITECTOS

PROYECTO
Av. Paseo Colon 735

OBRA
Edificio de Viviendas

UBICACIÓN
San Telmo


PLANO
Planta 1° / 12° - Depto A


ESCALA
1:50

FECHA
12/08/2026

PLANO N°
A - 07

REVISIÓN
R00

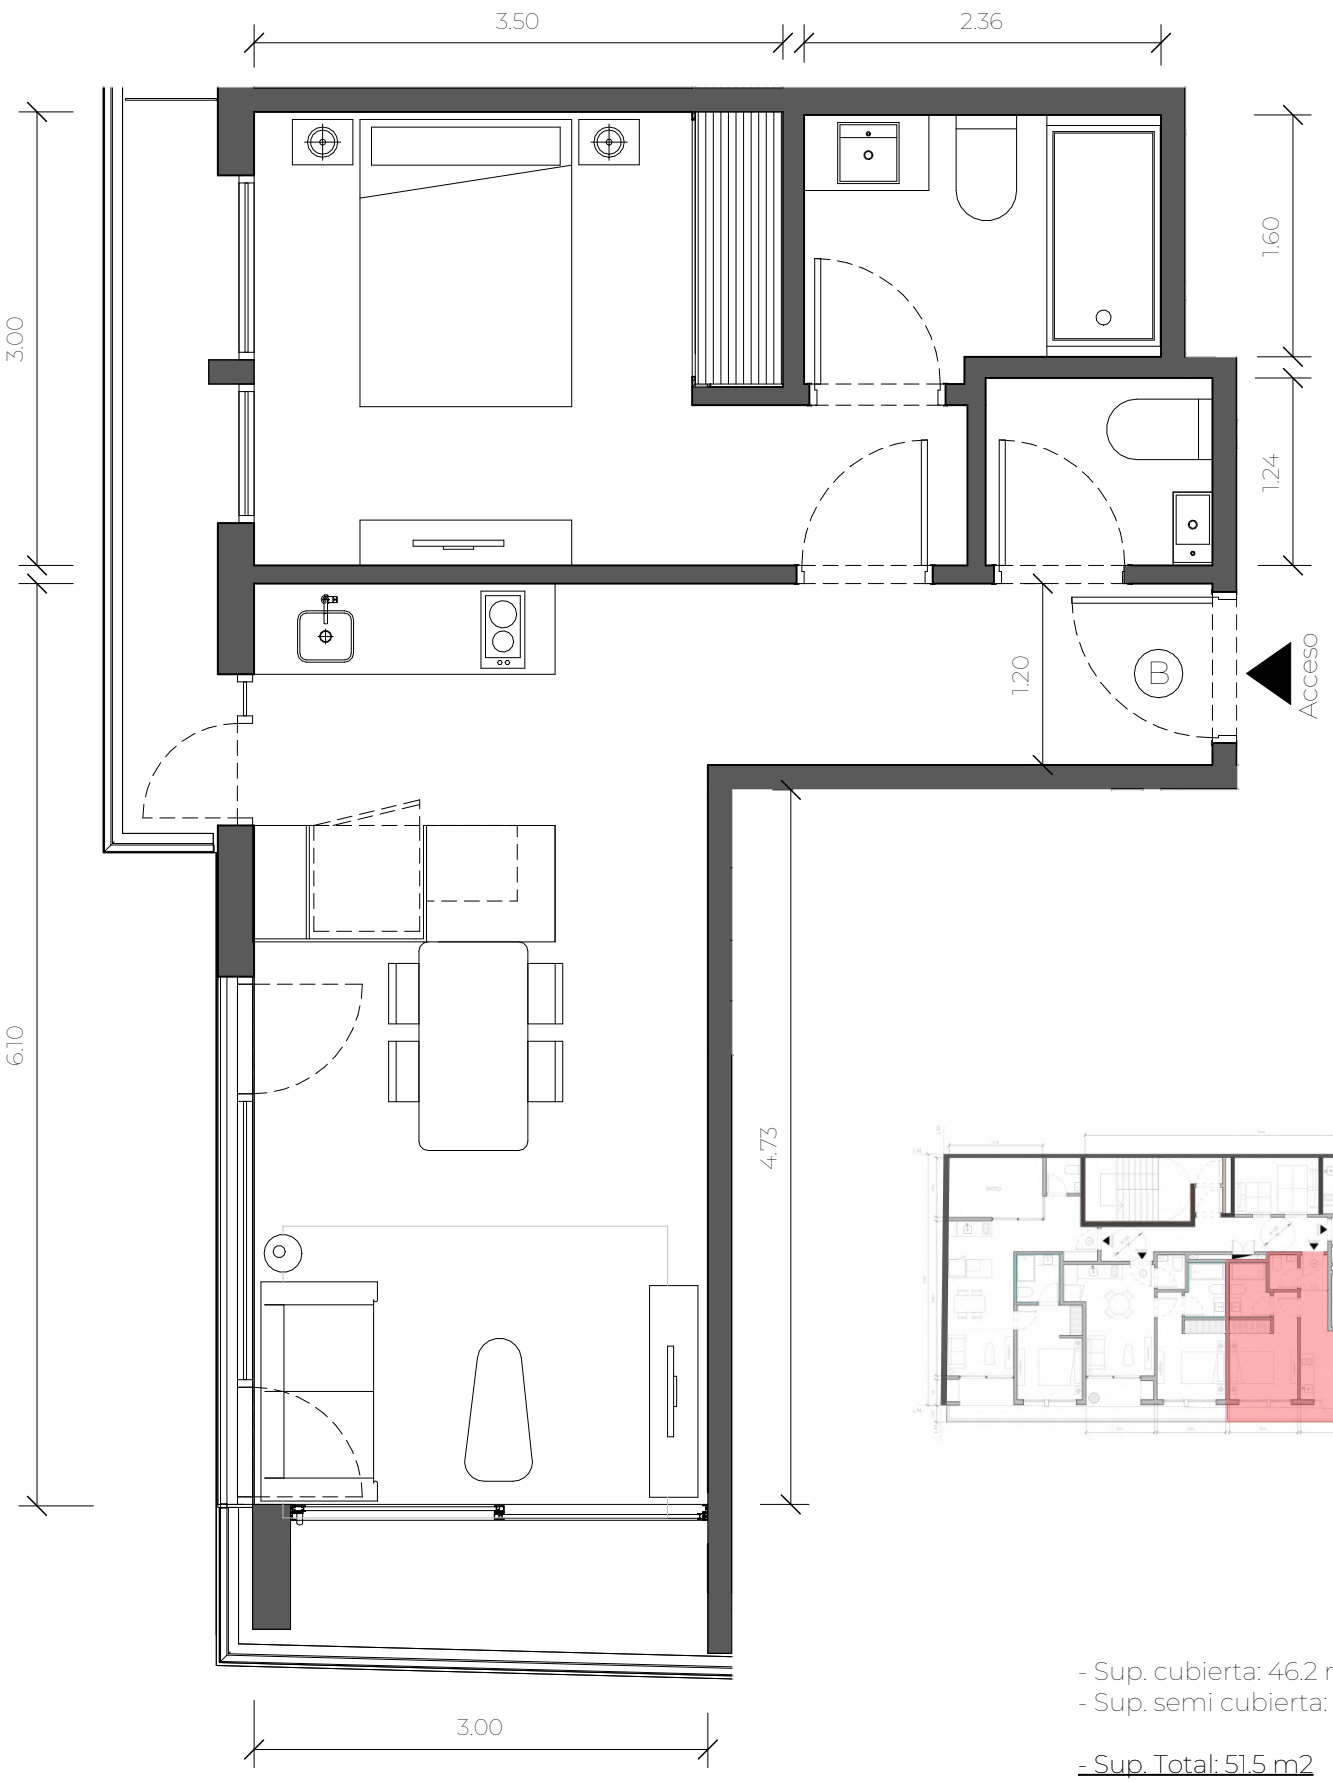

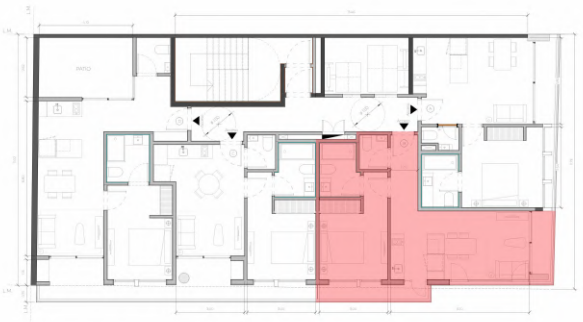

- Sup. cubierta: 46.2 m2
- Sup. semi cubierta: 5.3 m2

- Sup. Total: 51.5 m2

Cantidad: 12

CANEVA
ARQUITECTOS

PROYECTO
Av. Paseo Colon 735

OBRA
Edificio de Viviendas

UBICACIÓN
San Telmo


PLANO
Planta 1°/12° - Depto B

ESCALA
1:50

FECHA
12/08/2026

PLANO N°
A - 08

REVISIÓN
R00

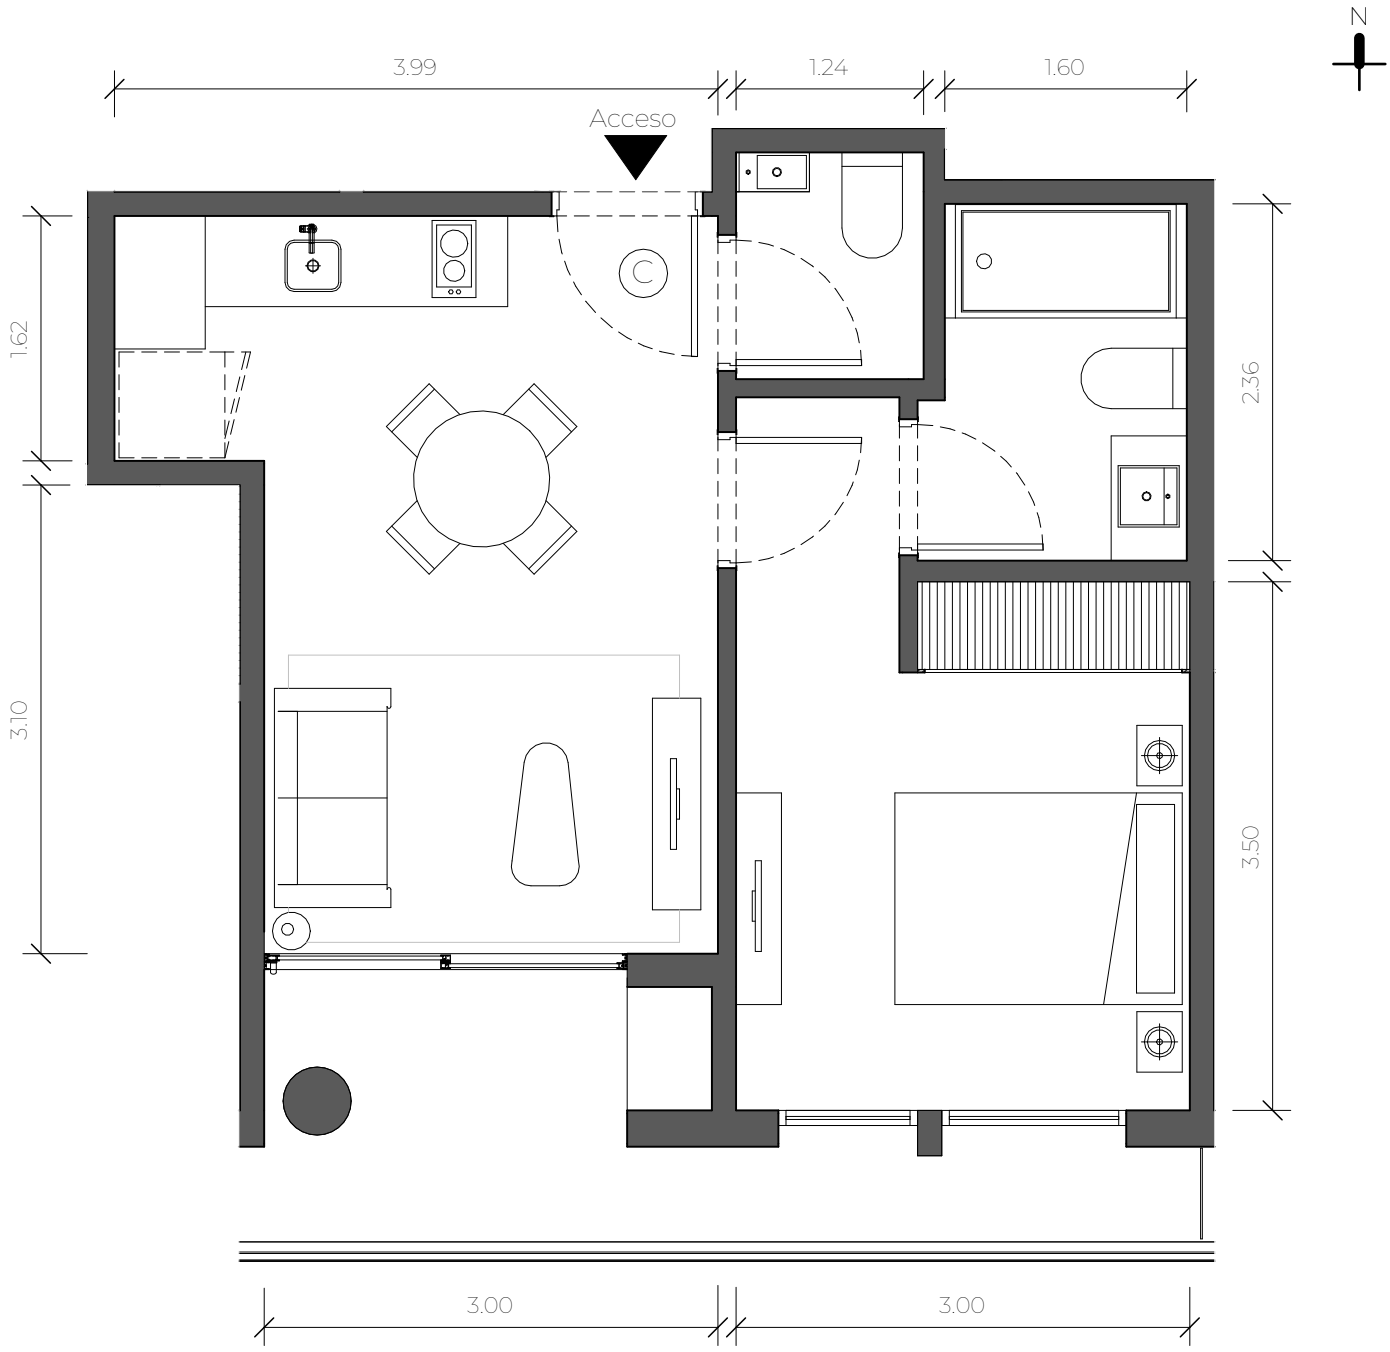



- Sup. cubierta: 38.8 m2
- Sup. semi cubierta: 7.0 m2

- Sup. Total: 45.8 m2

Cantidad: 1

CANEVA
ARQUITECTOS

PROYECTO
Av. Paseo Colon 735

OBRA
Edificio de Viviendas

UBICACIÓN
San Telmo


PLANO
Planta 1° - Depto C


ESCALA
1:50

FECHA
12/08/2026

PLANO N°
A - 09

REVISIÓN
R00

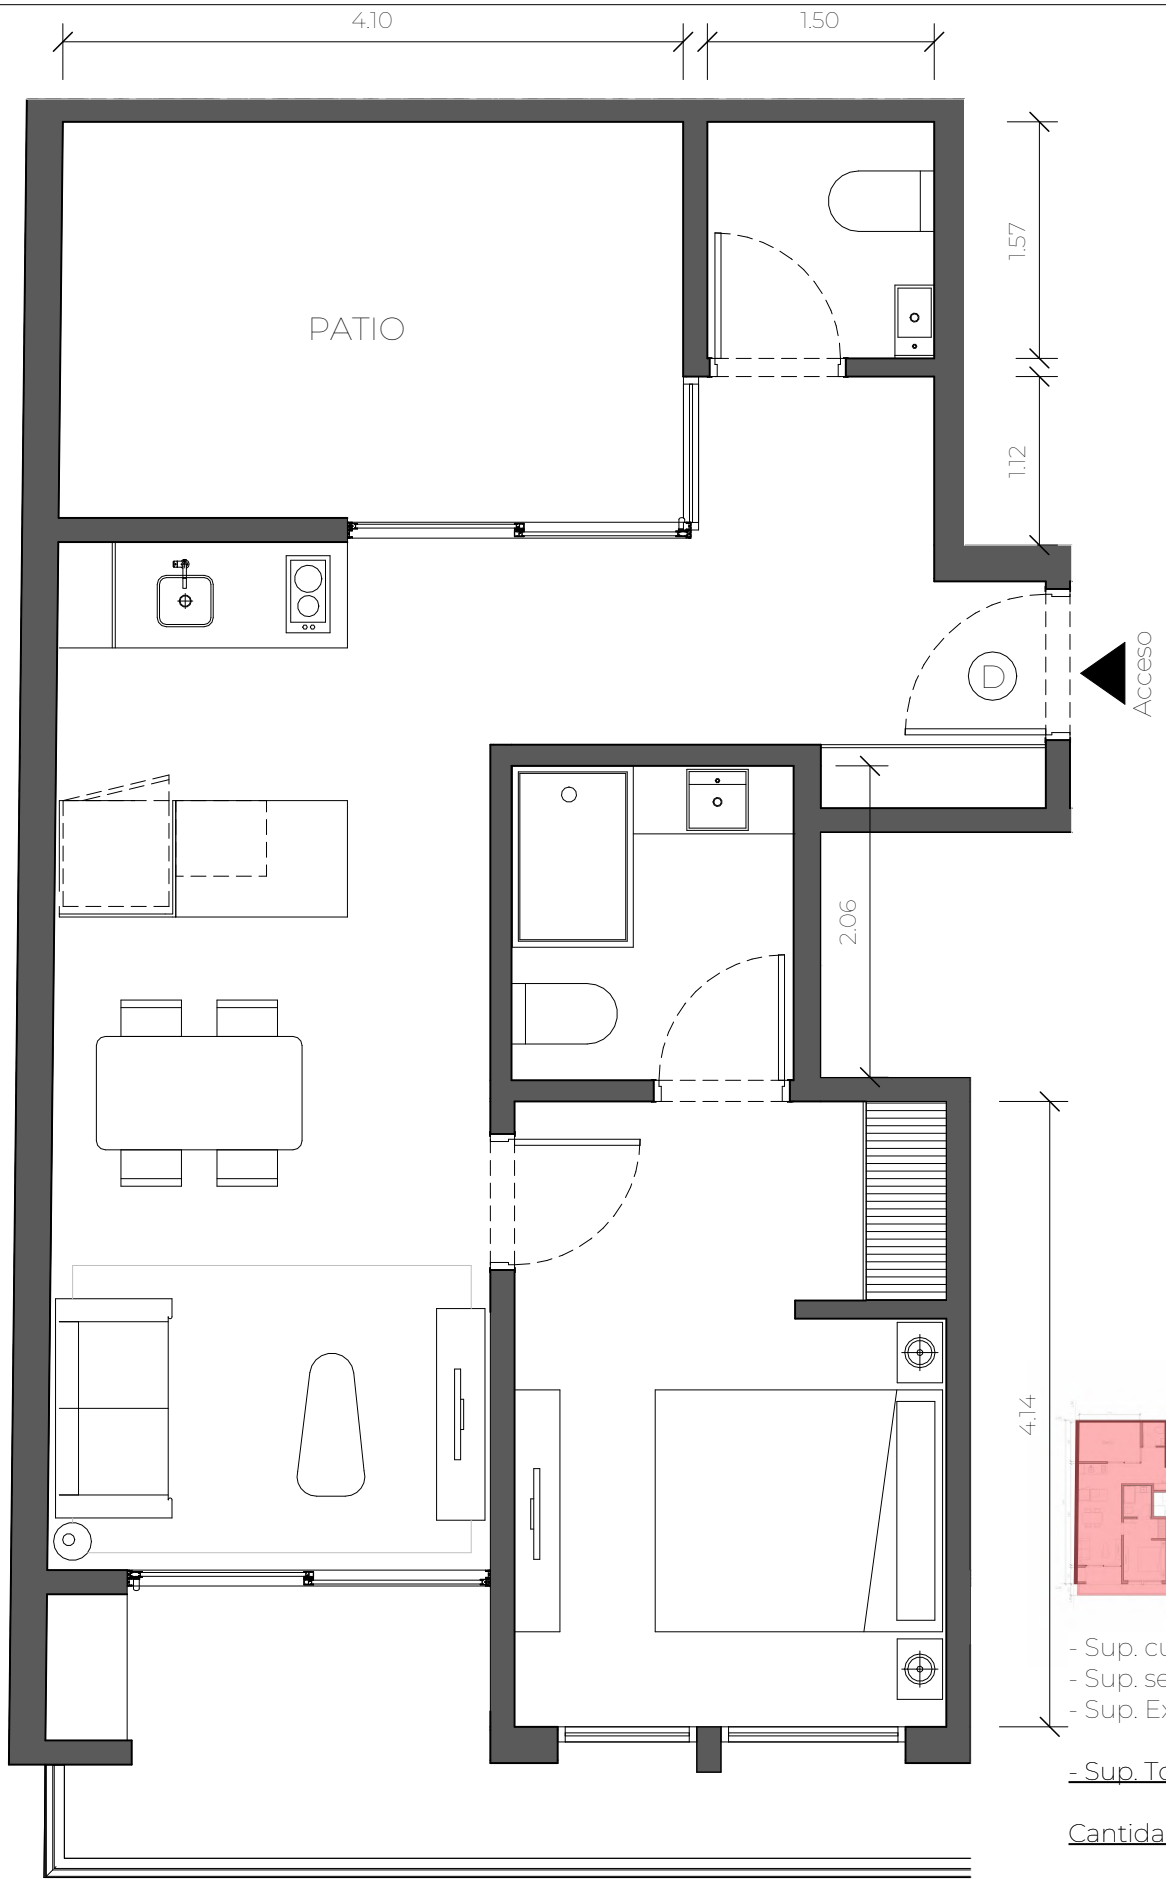

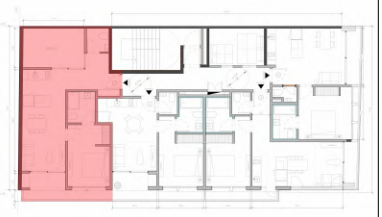

- Sup. cubierta: 52.0 m2
- Sup. semi cubierta: 8.1 m2
- Sup. Exterior: 12.1 m2

- Sup. Total: 72.2 m2

Cantidad: 1

2.93 | 2.86

CANEVA
ARQUITECTOS

PROYECTO
Av. Paseo Colon 735

OBRA
Edificio de Viviendas

UBICACIÓN
San Telmo


PLANO
Planta 1° - Depto D

ESCALA
1:50

FECHA
12/08/2026

PLANO N°
A - 10

REVISIÓN
R00

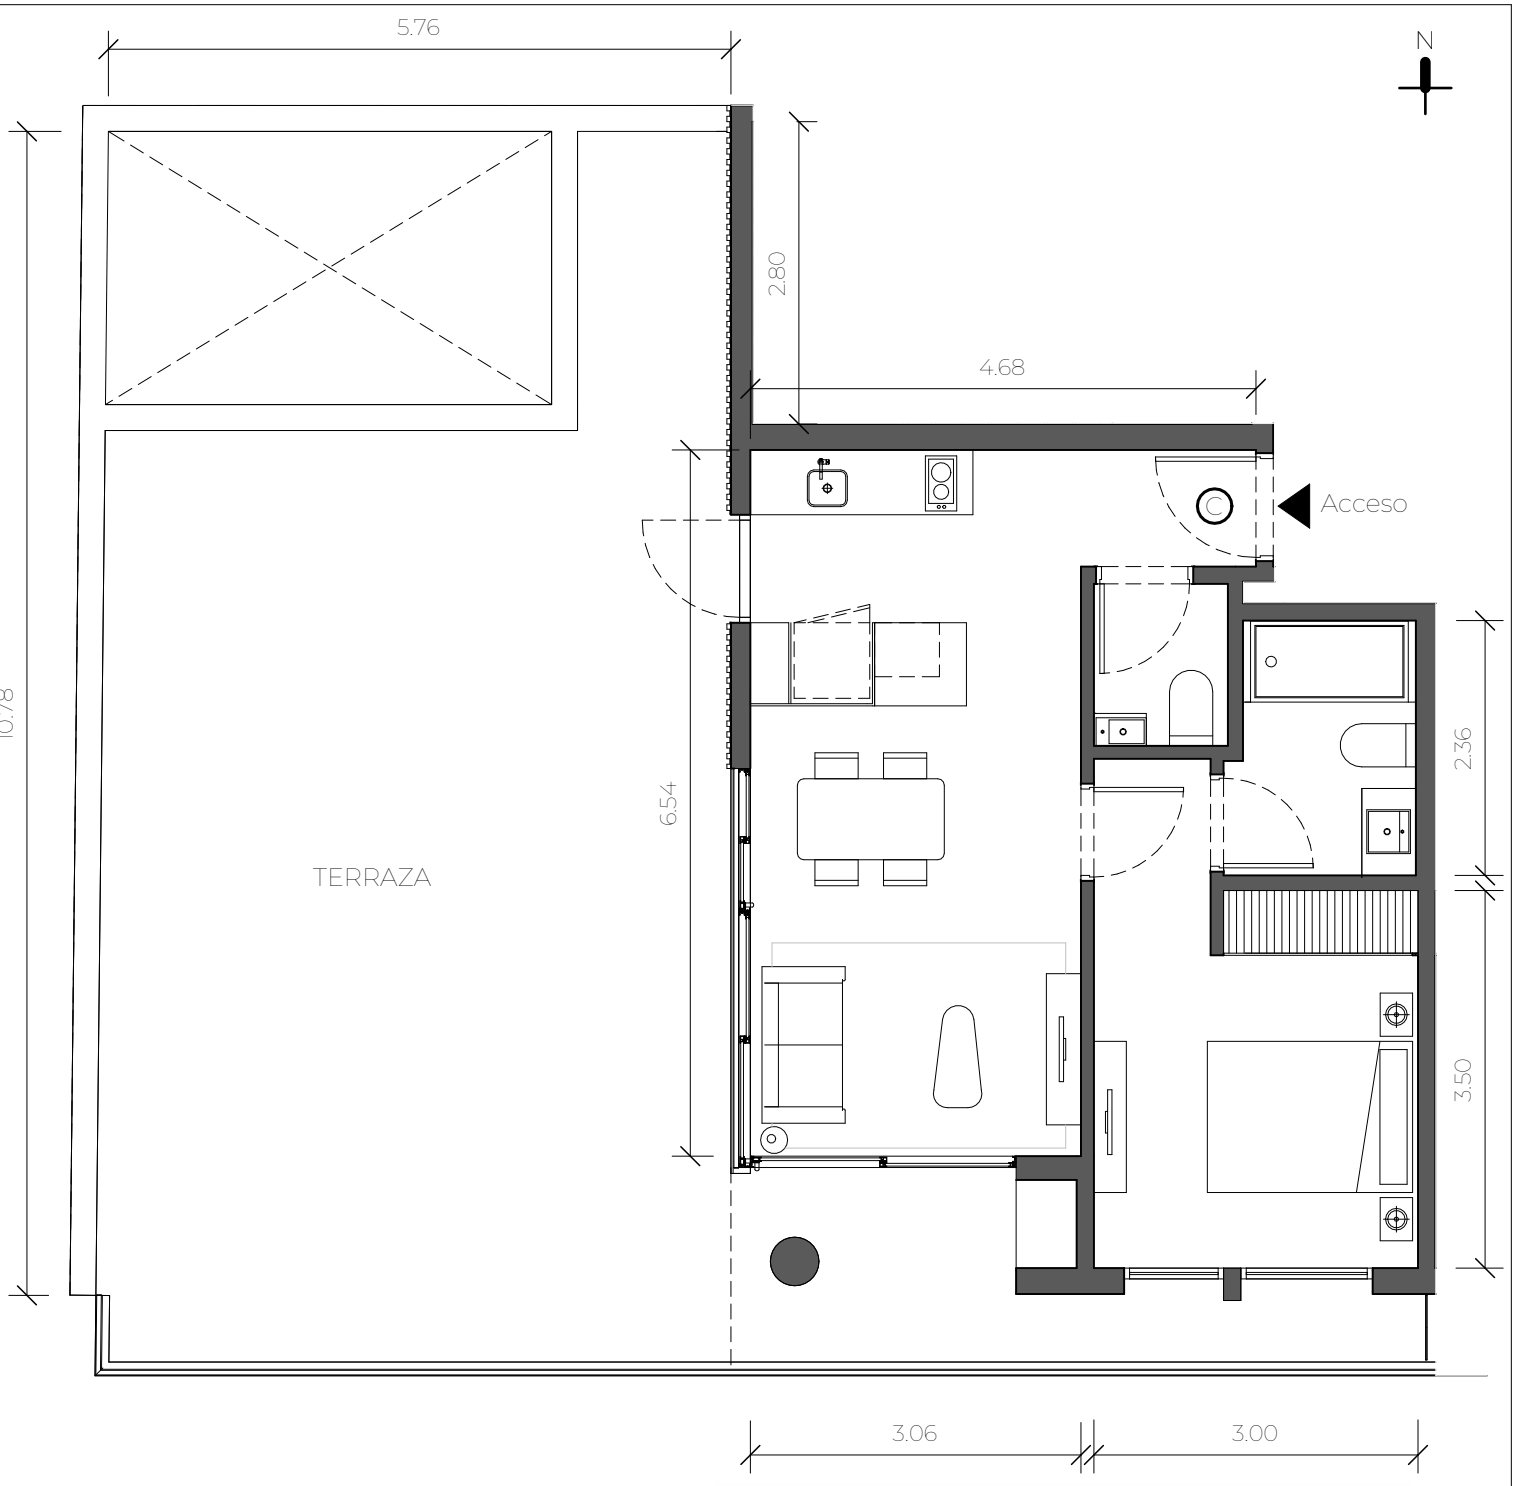



- Sup. cubierta: 45.0 m2
- Sup. semi cubierta: 8.5 m2
- Sup. Exterior: 57.3 m2

- Sup. Total: 110.8 m2

Cantidad: 1

CANEVA
ARQUITECTOS

PROYECTO
Av. Paseo Colon 735

OBRA
Edificio de Viviendas

UBICACIÓN
San Telmo


PLANO
Planta 2° - Depto C

ESCALA
1:70

FECHA
12/08/2026

PLANO N°
A - 11

REVISIÓN
R00

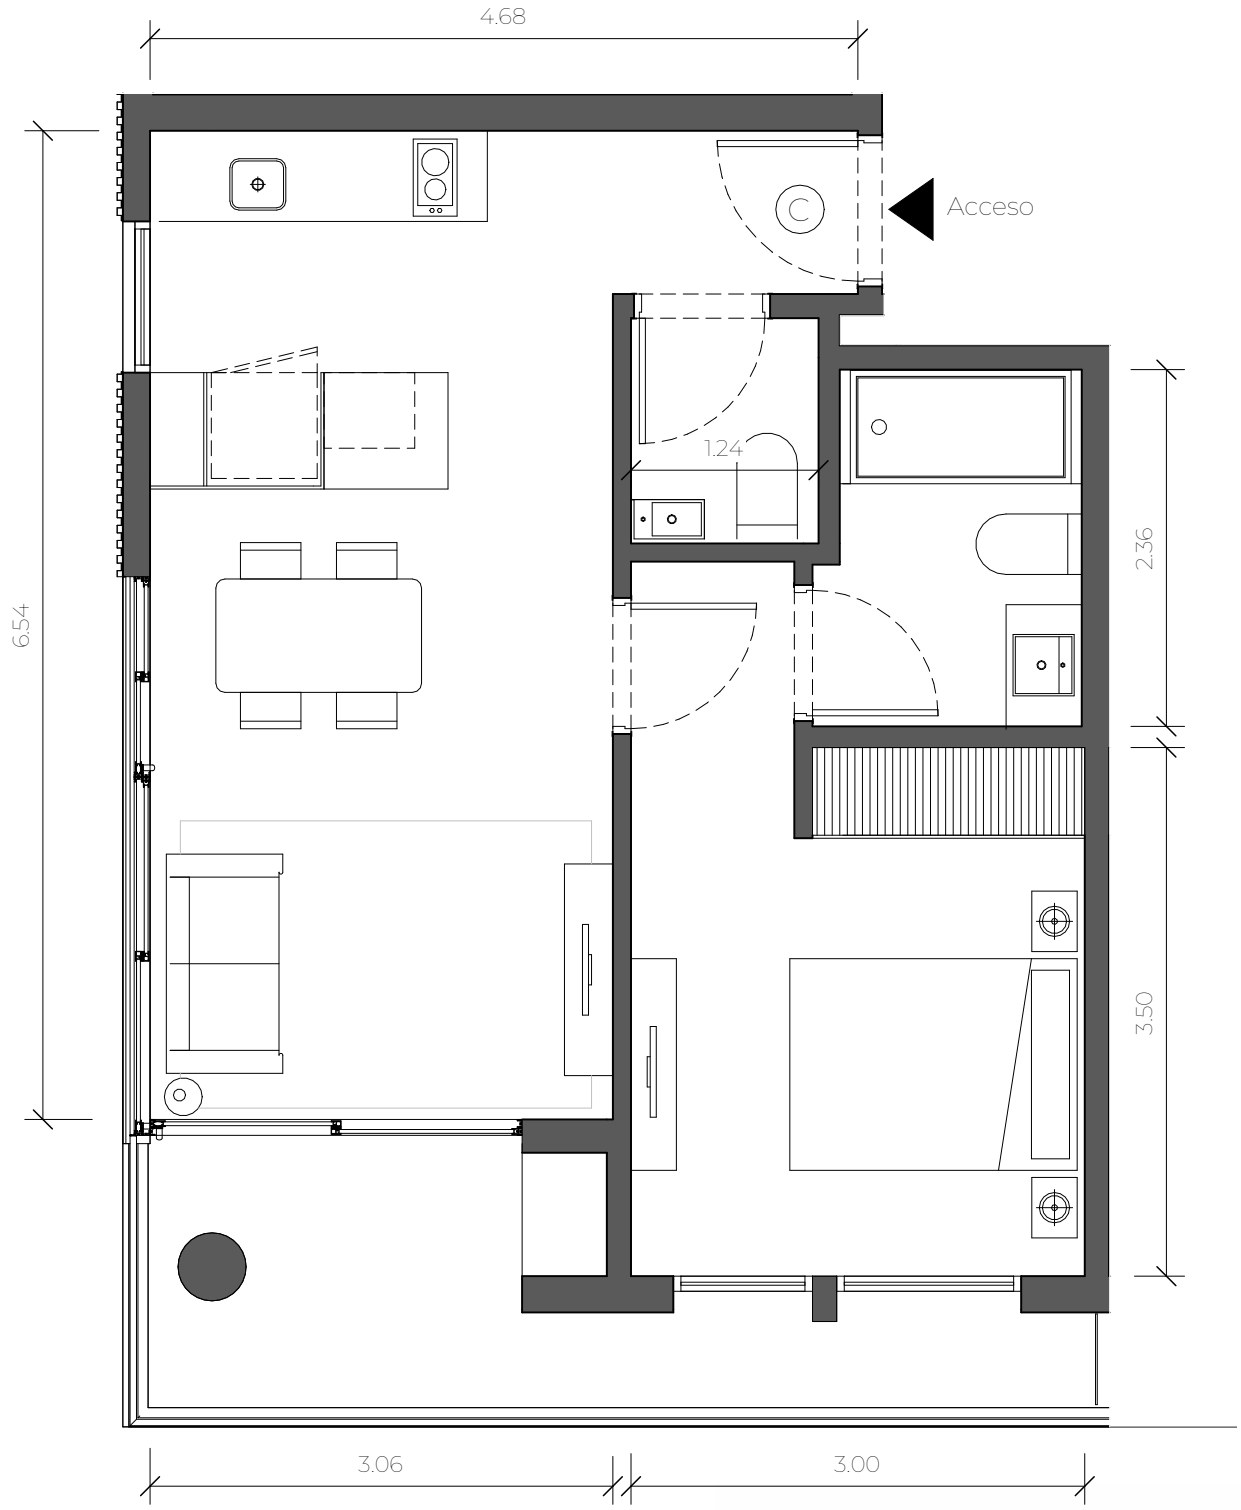



- Sup. cubierta: 45.2 m2
- Sup. semi cubierta: 8.2 m2

- Sup. Total: 53.4 m2

Cantidad: 10

CANEVA
ARQUITECTOS

PROYECTO
Av. Paseo Colon 735

OBRA
Edificio de Viviendas

UBICACIÓN
San Telmo


PLANO
Planta 3°/12° - Depto C

ESCALA
1:50

FECHA
12/08/2026

PLANO N°
A - 12

REVISIÓN
R00

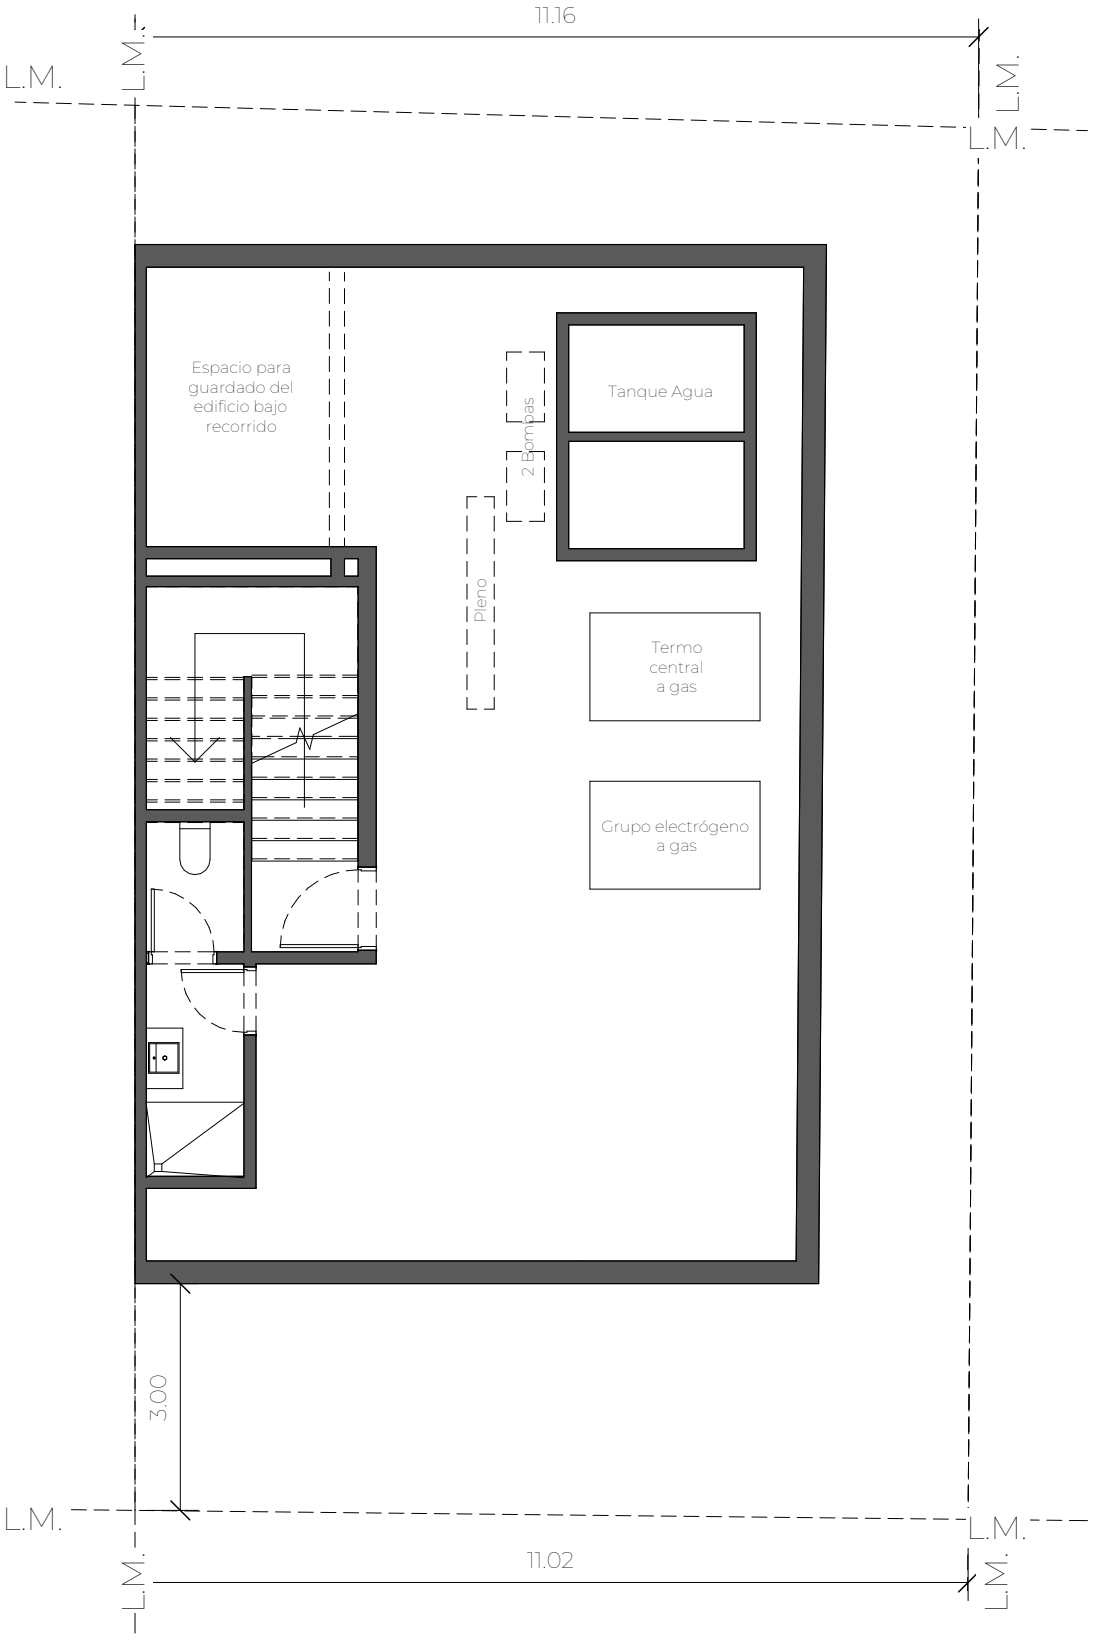

CANEVA

ARQUITECTOS

PROYECTO
Av. Paseo Colon 735

OBRA
Edificio de Viviendas

UBICACIÓN
San Telmo


PLANO
Planta Subsuelo

ESCALA
1:100


FECHA
12/08/2026

PLANO N°
A - 13

REVISIÓN
R00

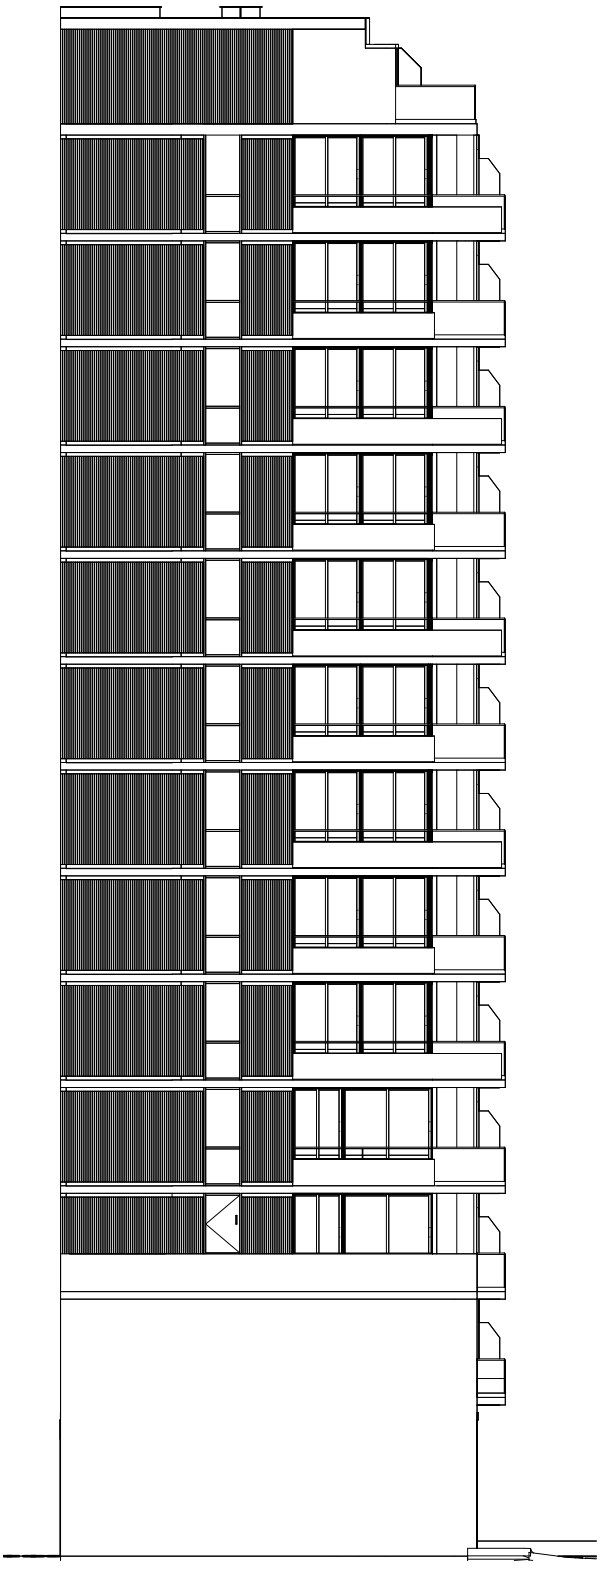

Vista Contrafrente

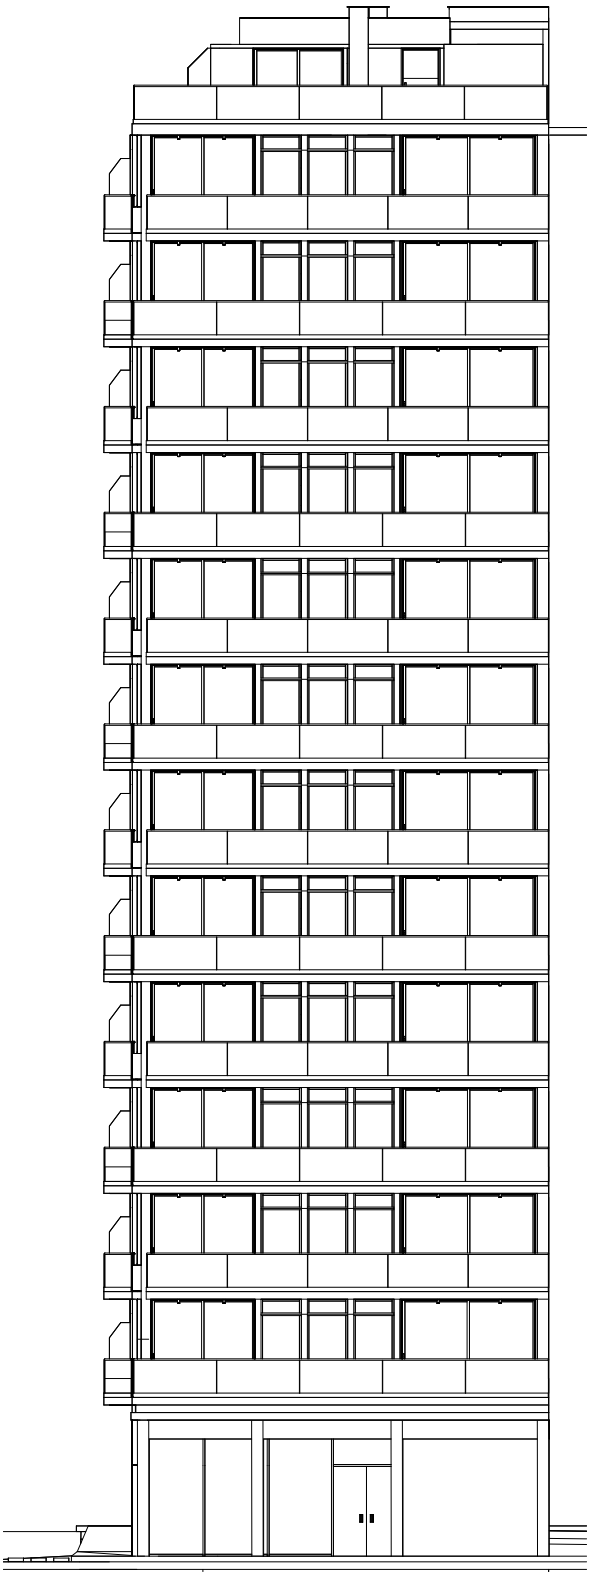

Vista Paseo Colon

CANEVA

ARQUITECTOS

PROYECTO
Av. Paseo Colon 735

OBRA
Edificio de Viviendas

UBICACIÓN
San Telmo


PLANO
Vistas

ESCALA
1:200

FECHA
12/08/2026

PLANO N°
A - 14

REVISIÓN
R00

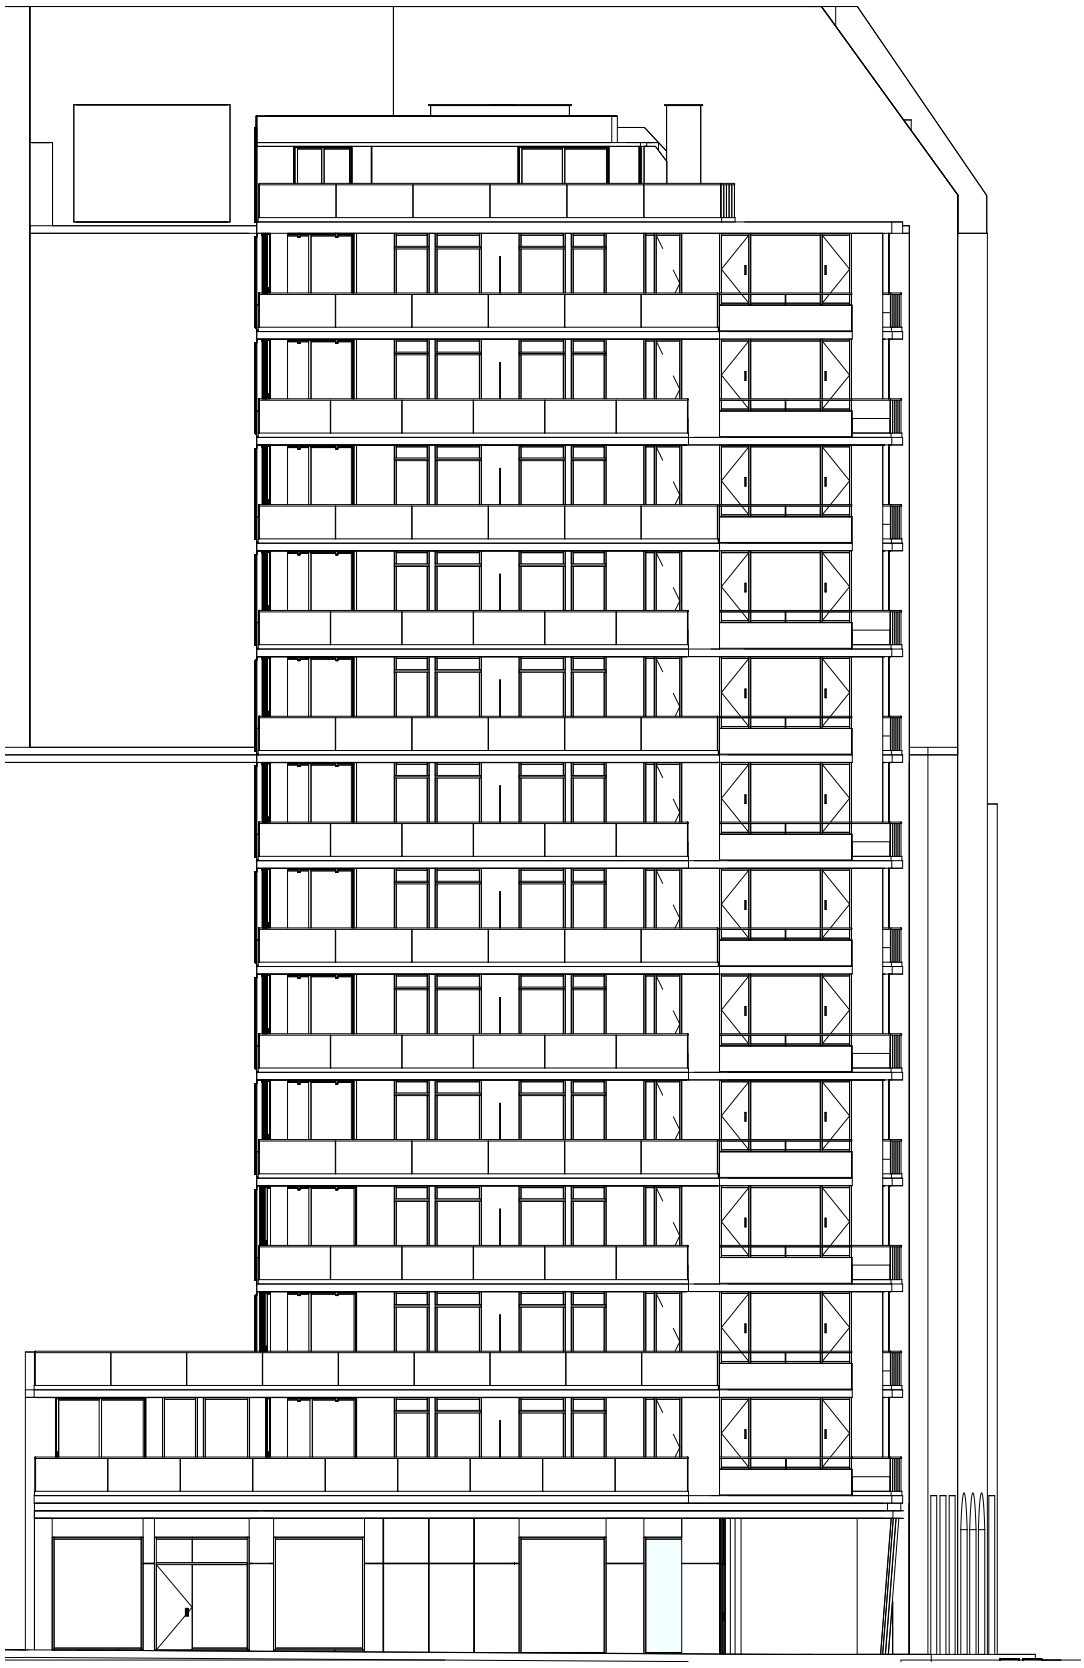

Vista San Lorenzo

CANEVA

ARQUITECTOS

PROYECTO
Av. Paseo Colon 735

OBRA
Edificio de Viviendas

UBICACIÓN
San Telmo

PLANO
Vistas

ESCALA
1:200

FECHA
12/08/2026

PLANO N°
A - 15

REVISIÓN
R00



CANEVA

ARQUITECTOS

PROYECTO
Av. Paseo Colon 735

OBRA
Edificio de Viviendas

UBICACIÓN
San Telmo

PLANO
Render

ESCALA
S/Esc

FECHA
12/08/2026

PLANO N°
A - 16

REVISIÓN
R00



Render Aereo - Frontal



Render Aereo

CANEVA

ARQUITECTOS

PROYECTO
Av. Paseo Colon 735

OBRA
Edificio de Viviendas

UBICACIÓN
San Telmo

PLANO
Render

ESCALA
S/Esc


FECHA
12/08/2026

PLANO N°
A - 17

REVISIÓN
R00



Render Aereo

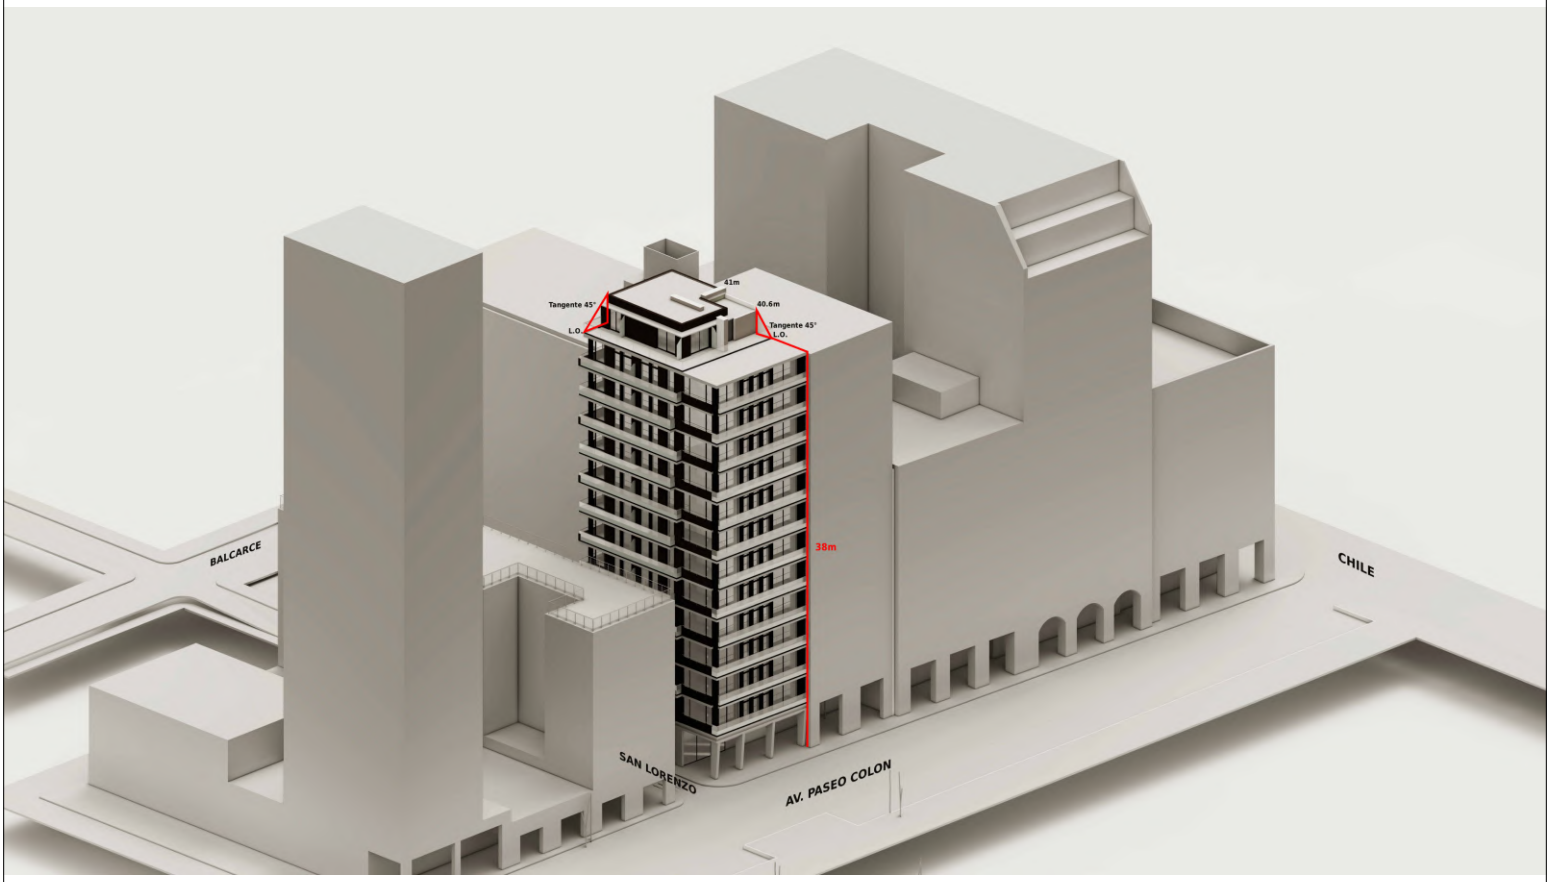

Axonometrica 3D

CANEVA
ARQUITECTOS

PROYECTO
Av. Paseo Colon 735

OBRA
Edificio de Viviendas

UBICACIÓN
San Telmo

PLANO
Render

ESCALA
S/Esc

FECHA
12/08/2026

PLANO N°
A - 18

REVISIÓN
R00


PASEO COLÓN 735

Informe de superficies y eficiencia - San Telmo, CABA


Proyecto aprobado | SS + PB + Pisos 1-13

SUPERFICIE TOTAL	VENDIBLE	COMÚN	FACTOR CONSTR./VEND.
2.751,876 m²	**2.039,287 m²**	**712,589 m²**	**1,349**
100%	74,11%	25,89%	m²/m²

DISTRIBUCIÓN POR NIVEL

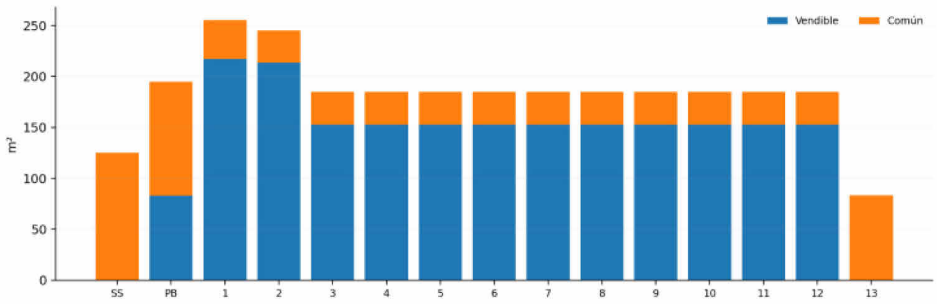

COMPOSICIÓN

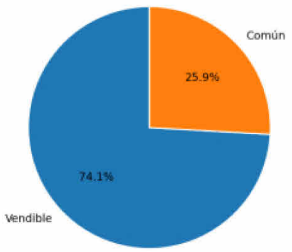

La superficie vendible representa el 74,11% del total computado,

INDICADORES DE EFICIENCIA

Eficiencia global: 74,11% vendible / 25,89% común,
Cada 1,00 m² vendible requiere 1,349 m² de superficie total construida,
Plantas 3 a 12: 152,590 m² vendibles + 32,220 m² comunes = 184,810 m².
Eficiencia de la planta repetitiva (pisos 3 a 12): 82,57%,
Los niveles SS, PB y Piso 13 concentran superficie no vendible y reducen la eficiencia global.

CUADRO DE SUPERFICIES

Nivel	Vendible	Común	Total	% vendible	Incidencia total
SS	0,000	125,054	125,054	0,0%	4,5%
PB	82,846	112,154	195,000	42,5%	7,1%
1	216,997	38,132	255,129	85,1%	9,3%
2	213,544	31,831	245,375	87,0%	8,9%
3	152,590	32,220	184,810	82,6%	6,7%
4	152,590	32,220	184,810	82,6%	6,7%
5	152,590	32,220	184,810	82,6%	6,7%
6	152,590	32,220	184,810	82,6%	6,7%
7	152,590	32,220	184,810	82,6%	6,7%
8	152,590	32,220	184,810	82,6%	6,7%
9	152,590	32,220	184,810	82,6%	6,7%
10	152,590	32,220	184,810	82,6%	6,7%
11	152,590	32,220	184,810	82,6%	6,7%
12	152,590	32,220	184,810	82,6%	6,7%
13	0,000	83,218	83,218	0,0%	3,0%

CANEVA
ARQUITECTOS

PROYECTO
Av. Paseo Colon 735

OBRA
Edificio de Viviendas

UBICACIÓN
San Telmo

PLANO
Resumen

ESCALA
S/Esc

FECHA
12/08/2026

PLANO N°
A - 19

REVISIÓN
R00